


图例	名称
	吊灯
	吸顶灯
	壁灯
	暗藏式铝槽灯
	镜前灯
	可调角度射灯（暗装）
	隐藏式节能筒灯（暗装）
	防潮筒灯（暗装）
	双头射灯（明装）
	磁吸轨道灯（暗装）
	空调风口
	空调出风口
	空调回风口
	300*600浴霸

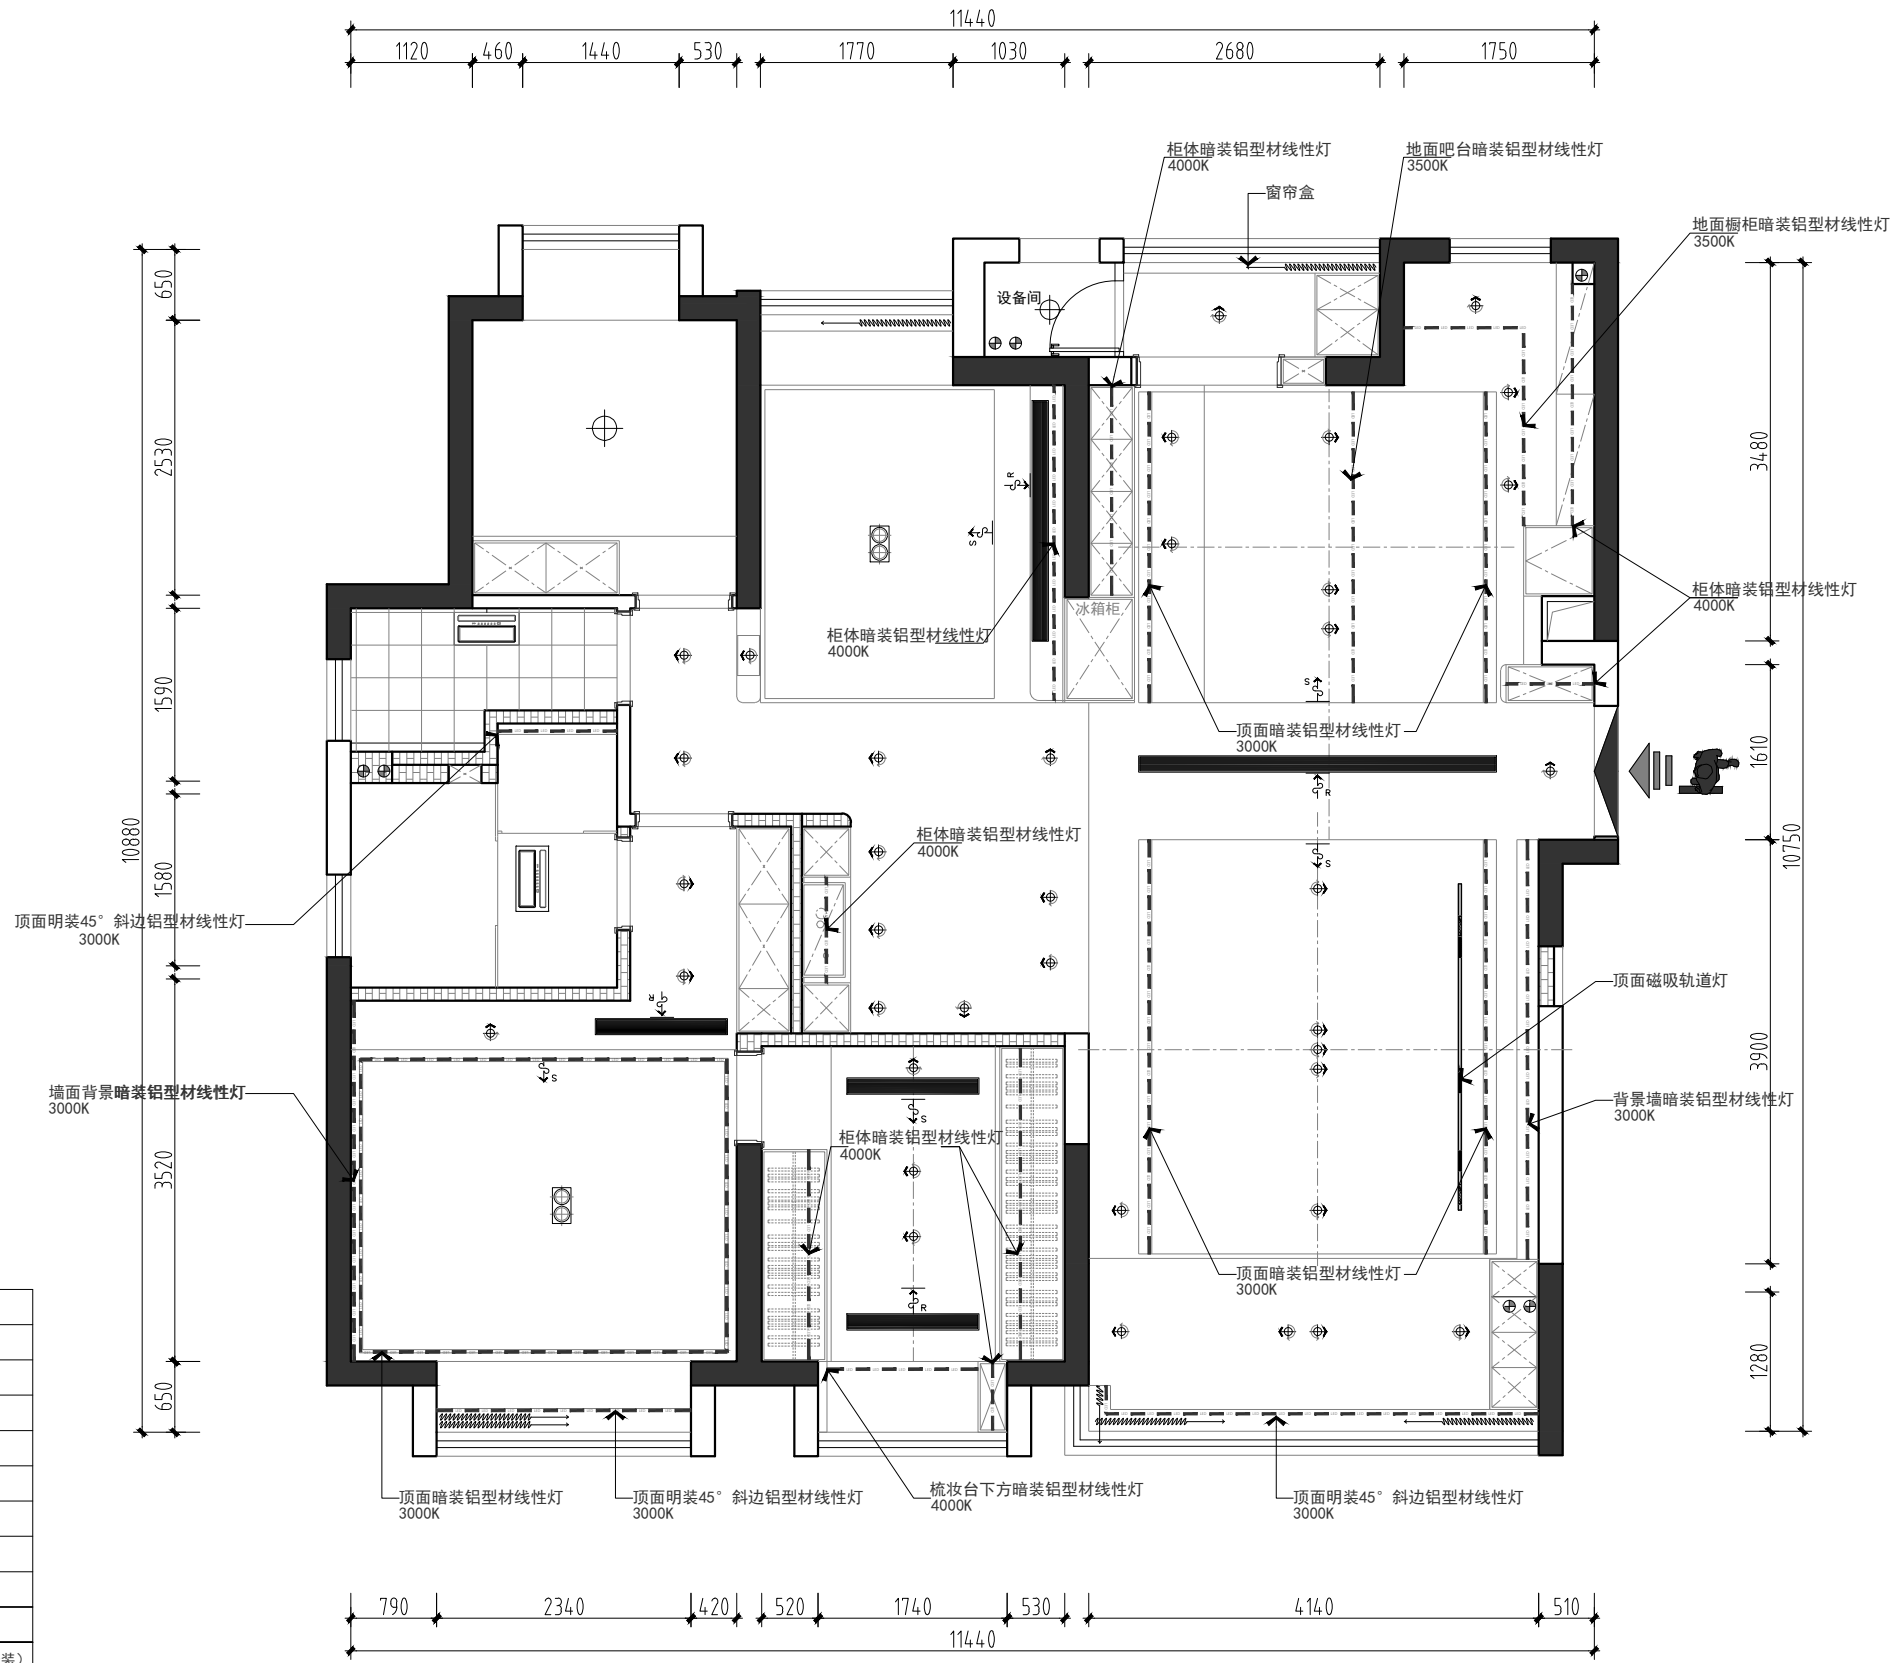

墙顶面辅助光源示意图
SCALE 1:60@A2

灰色系空间设计
Grey System Design Space Design

灰色系空间设计有限公司
Grey System Design Space Design
地址：长沙市天心区劳动西路245号凯瑞大厦1703
电话：0731-85492800
TEL：0731-85492800

阳光城-溪山悦

项目名称

本设计之知识产权属灰色系空间设计有限公司任何复制或传播，均需获得书面授权。
INTELLECTUAL PROPERTY IN THE DESIGN OF THE GENUS WILSPACE DESIGN LIMITED COMPANY OF ANY COPY OR USE, ARE REQUIRED TO OBTAIN WRITTEN AUTHORIZATION.

备注

审核		
制图		
设计		
项目变更		
比例	1:60@A2	
日期	2025.10	
项目编号		

图纸名称

BL-06

图号	06
DRAWING NO	